

HEADQUARTERS, DHAKA

Tigotek HQ

A three-floor office built for a marketplace.

Public at the base. Production in the middle. Focus at the top. A stacking strategy, three scaled floor plans, a room schedule and the standards behind them, drawn from the founder's hand sketch and upgraded to industry practice.

12,594

sq ft gross over 3 floors
1,170 m², 4,198 sq ft per floor

52

assigned desks
plus 28 café seats for partners


100

people at a town hall
forum with stage and step seating

33

meeting-room seats
5 rooms, plus 8 pods

PREPARED FOR	Al Fuad Hassan, Founder and CEO
DATE	4 October 2026
STATUS	Concept for discussion. Not for construction.
BASIS	Founder's sketch, plus an assumed 26 x 15 m floor plate (assumptions on page 8).

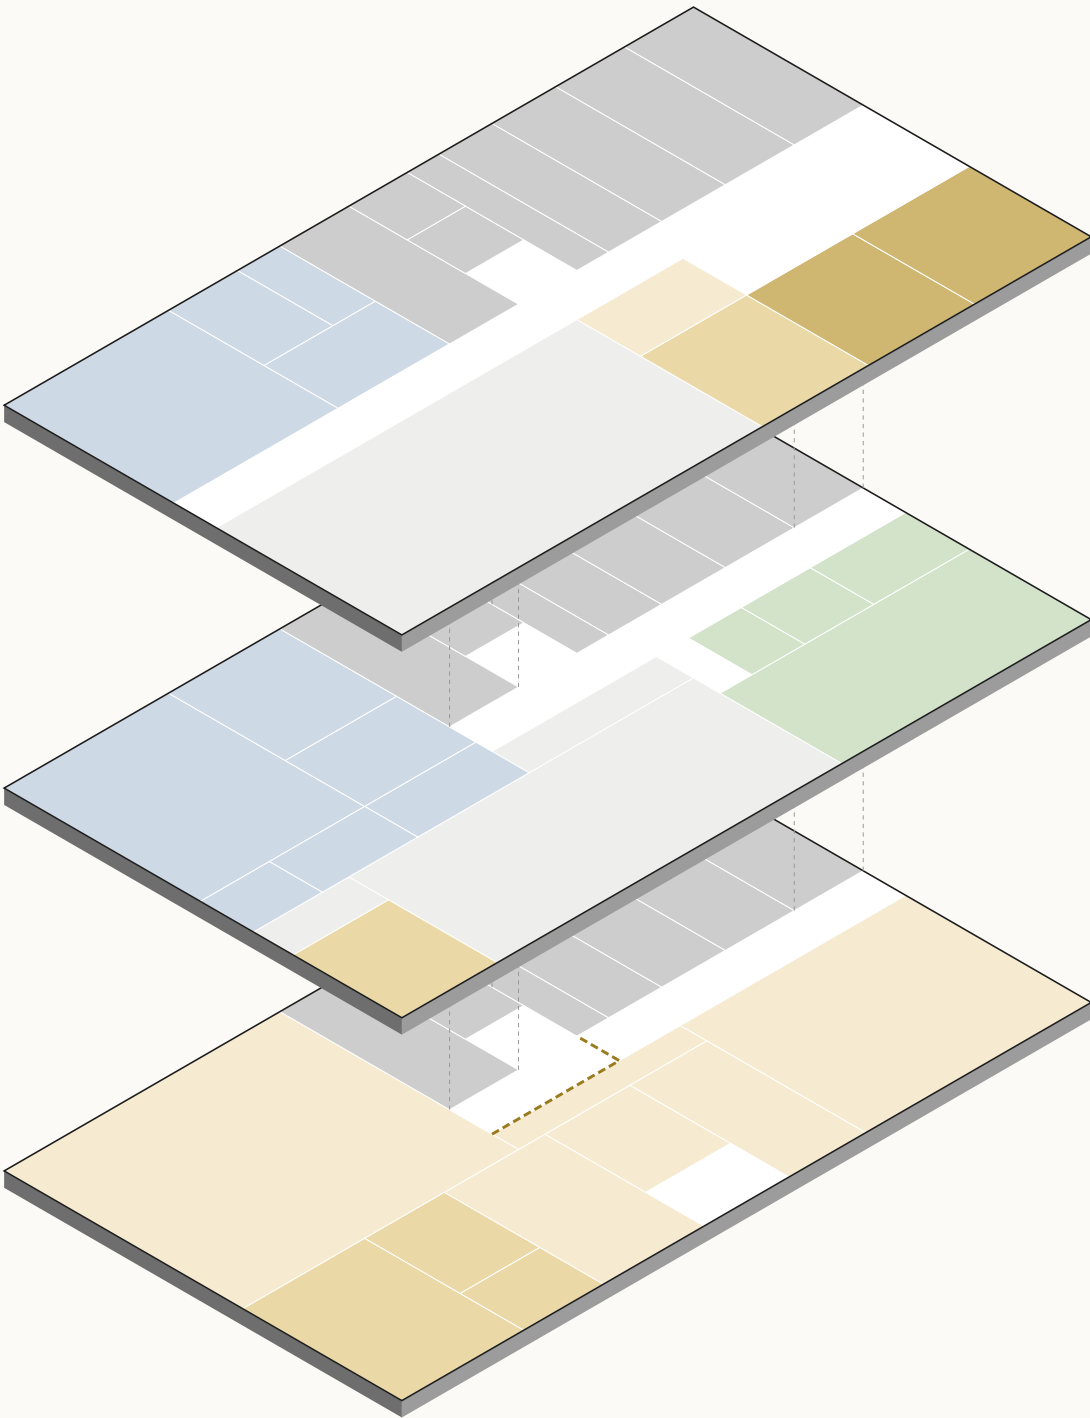

Exploded stack, ground floor at the bottom

- Community & hospitality

Meet & collaborate

Workspace

Studio & tech ops
- Leadership

Quiet & wellbeing

Core & services

What changed, and why

Your sketch gets the stacking instinct right. The scheme keeps it and fixes four things: who can go where, where the noise goes, what the building legally needs, and which rooms were the same room twice.



Founder's sketch. Read as a stack: the top band is Level 2, the bottom band is the ground floor.

HOW THE SKETCH WAS READ

Floor	Written on the sketch
Level 2	Technical lead Engineers Technicians Engineers Pods / waiting room Conference CEO Director room
Level 1	Studio / Marketing / Conference Stages Other studio arrangements / soundproof room Thinking room / Reading room
Ground	Lobby / nice sitting place / big ceiling and pods Café, networking
Note	Two words are hard to read: the third bay on Level 2 is taken as Technicians and the top-right room as CEO. The line “We are going to be the next Fiverr / Upwork” is treated as the brief.

NET EFFECT

9 kept and upgraded 2 moved down to G 4 removed or merged 5 added not on the sketch

THE BRIEF BEHIND THE SKETCH

“We are going to be the next Fiverr / Upwork.”

A marketplace HQ has three jobs: earn client trust at the door, give the partner network a home, and let the in-house team ship fast. Every change on this page serves one of those three.

KEPT AND UPGRADED

Engineers x 2

Two squads, 24 desks. Clusters run at right angles to the glass so no screen faces a window. A phone pod closes every cluster.

Technicians

Tech Ops suite: 6-seat NOC with video wall, tech bench, MDF comms room and IT store. Glass to the corridor so escorted clients see the operation.

CEO, Director

Kept on the quiet top floor and right-sized (20 m² and 18 m²). Glazed fronts with blinds, EA desk outside.

Conference on L2

Becomes the war room: 8 seats, whiteboard walls, beside the squads.

Studio, soundproof room, studio extras

One isolated Content Studio suite: cyc studio, podcast booth, shared control room, green room, kit store, one controlled door.

Marketing, Conference on L1

Creative and media studio with 16 desks, a pin-up wall and a 6-seat review room.

Thinking room, reading room

One library. Quiet, no calls, daylight on two sides.

Lobby, sitting place, pods, big ceiling

Arrival hall with host desk and two meeting pods. Ground floor set at 4.5 m floor to floor.

Café, networking

Work café: coffee bar, 28 seats with power, partner lockers on the brand wall.

MOVED

Stage: L1 to ground

Now the Forum: stage, LED wall, 3-tier step seating with chair storage underneath. Events stay on the public floor and 100 guests leave at street level.

Client meetings: L2 to ground

Client suite at arrival: boardroom, meeting room, interview room. Visitors stop at the security line unless escorted.

REMOVED

Waiting room on L2

It duplicates the ground floor lobby.

Tech lead's closed room

The lead sits with both squads. The war room covers ceremonies and one-to-ones.

Separate thinking and reading rooms

One library does both jobs.

Stand-alone soundproof room

Absorbed into the studio suite.

ADDED: MISSING FROM THE SKETCH

Security

Host desk, speed gates and one security line in front of the lift and Stair 1.

Code and safety

Two protected stairs, a lift and an accessible WC on every floor.

Faith and wellbeing

Prayer rooms for men and women with wudu, plus a lockable wellness / parent room.

Daily support


Tea point on L1, pantry on L2, electrical / IPS room, MDF comms room, IT store.

Marketplace kit

Interview / vetting room for partner assessments, partner lockers, power at every café seat.

Three floors, one rule

The higher you go, the more private and focused it gets. Strangers stay low, deep work goes high.

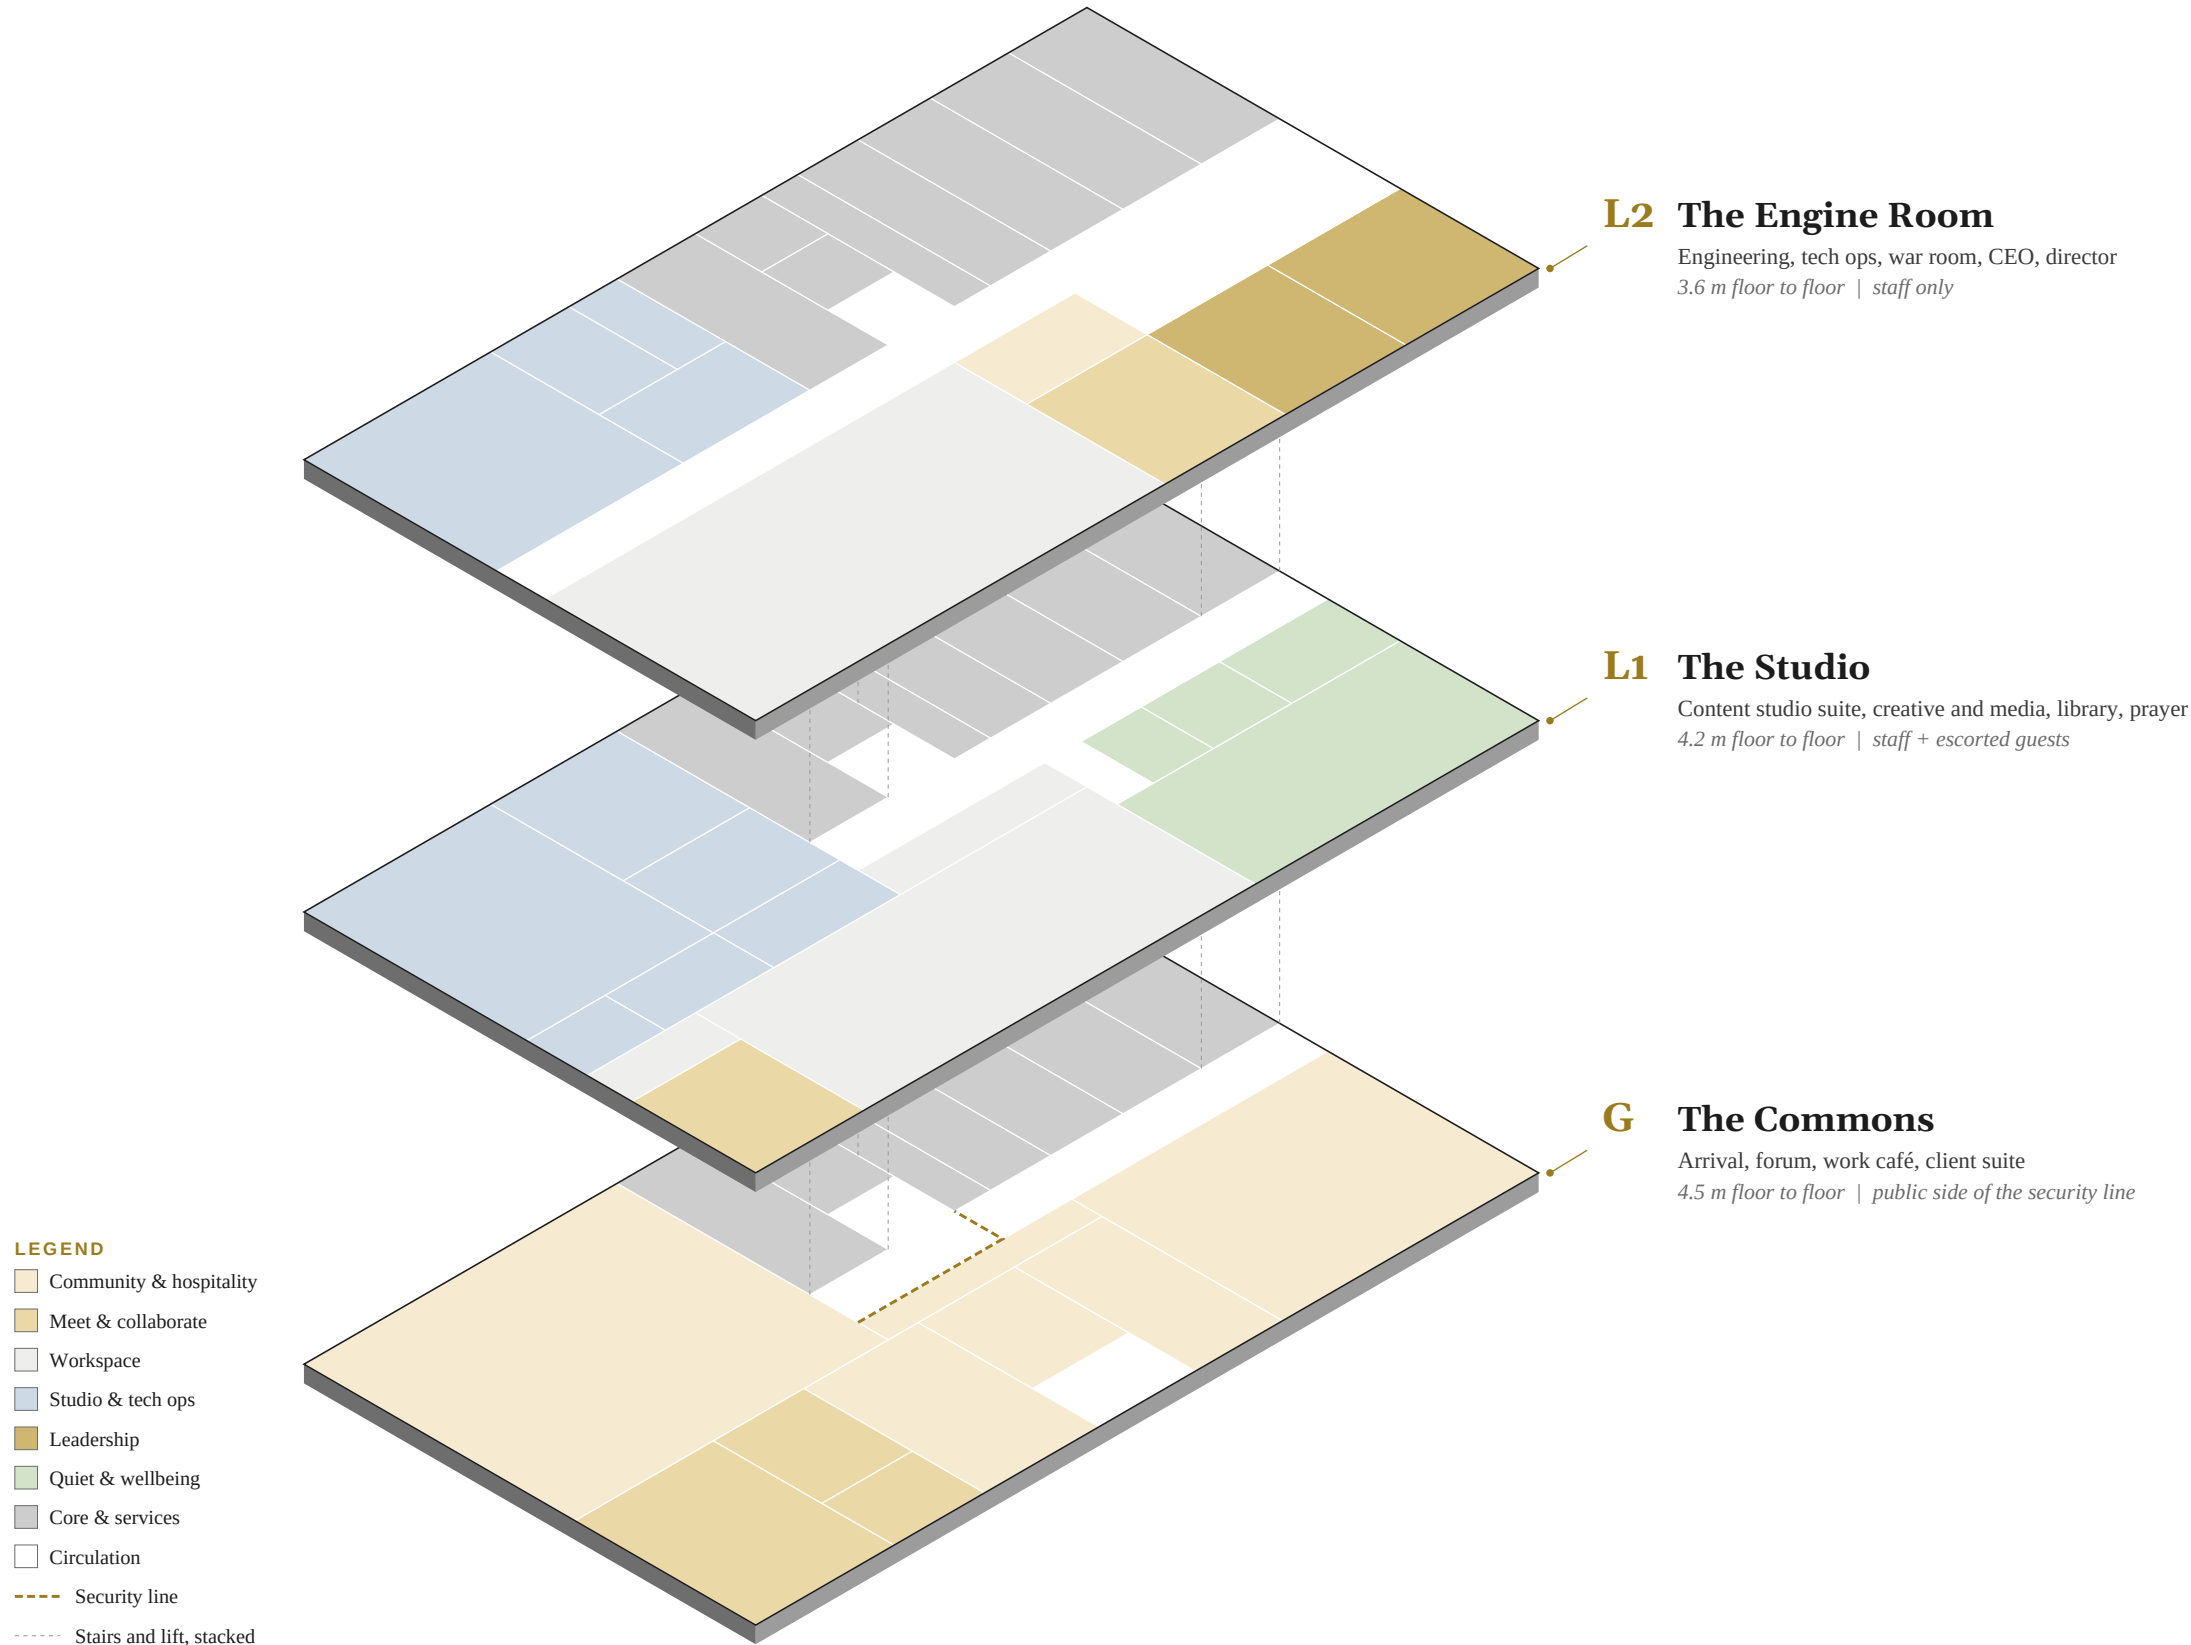

SIX DESIGN RULES

- 1 Privacy gradient.** Public at G, production at L1, focus and leadership at L2.
- 2 One security line.** Speed gates guard the lift and Stair 1. Visitors, partners and event guests stay on G unless escorted.
- 3 Zone the noise.** Studio and forum sit away from desks. The core and the library buffer the studio from focus work.
- 4 Stack the services.** Stairs, lift, WCs and risers sit in one rear core, identical on every floor. Plumbing stacks, floors stay flexible.
- 5 Daylight to people.** Desks run along the glass. Studio, MDF and stores take the blind side.
- 6 Build for the marketplace.** Vetting room, partner lockers and powered café seats make G the physical home of the partner network.

WHO GOES WHERE

Who	G	L1	L2
Staff	Yes	Yes	Yes
Clients	Yes	Escorted	Escorted
Partners, freelancers	Yes	Escorted	No
Event guests	Forum, café	No	No
Podcast, shoot guests	Arrival	Studio via green room	No
Couriers	Host desk	No	No

Cards open the speed gates. The studio suite and tech ops add their own card and PIN.

SECTION HEIGHTS

Floor	Floor to floor	Why
L2	3.6 m	Standard office, about 2.9 m clear
L1	4.2 m	Studio needs about 3.5 m clear
G	4.5 m	The big ceiling: forum, café, arrival

The Commons



ROOM SCHEDULE			
No.	Room	m²	Use / capacity
1	Arrival hall + reception	60	host desk, 2 meeting pods
2	Forum / town hall	94	~75 seated, ~100 with lobby
3	Work café	60	28 seats, power at every seat
4	Boardroom	28	10 seats
5	Meeting	11	6 seats
6	Interview / vetting	7	3 seats, partner assessments
Core: stairs, lift, WCs, services		95	identical on every floor
Corridors and lobbies		36	

FLOOR DATA	
Gross floor area	390 m² (4,198 sq ft)
Usable, excluding core	295 m²
Floor to floor	4.5 m
Desks on this floor	1

- DESIGN MOVES**
- Door to lift in a straight line.** The host desk faces west, so one person sees the entrance and the speed gates.
 - One room, two modes.** The forum is the lounge every day and the town hall on event days: stage, LED wall, step seating with chair storage underneath.
 - Clients never need a pass.** The client suite sits before the security line.
 - The network's front room.** Power at every café seat, partner lockers on the back of the brand wall.

- SPECIFICATION NOTES**
- Forum: dimmable DMX lighting, stage wash, LED wall with ceiling speakers, floor boxes for AV.
 - Café: espresso and grab-and-go only, so no kitchen extract. Hot and cold water, one sink, under-counter fridges.
 - Vestibule with auto doors holds the cool air in and the Dhaka dust out.
 - Boardroom built to STC 53 for video calls, interview room to STC 45. CCTV at doors, gates and café.

LEGEND

Community & hospitality

Meet & collaborate

Workspace

Studio & tech ops

Leadership

Quiet & wellbeing

Core & services

Circulation

Structure / core wall

Partition

Glazed partition

Acoustic wall (studio)

Door swing

Column, 5.2 m grid

KEY

L2

L1

G

SCALE 1:100 AT A3

0 1 2 3 4 5 m

Plate assumed 26 x 15 m on a 5.2 m grid. Refit to the real building once measured. Furniture indicative.

TIGOTEK HQ, DHAKA		CONCEPT
DRAWING	Ground floor plan: The Commons	
DRAWING NO.	TGT-HQ-A-101	
SCALE	1:100 at A3	
REVISION	P01, draft for discussion	
PREPARED FOR	Al Fuad Hassan, Founder and CEO	

The Studio



ROOM SCHEDULE			
No.	Room	m²	Use / capacity
1	Creative & media studio	87	16 desks, pin-up wall
2	Creative review	15	6 seats, colour-calibrated screen
3	Studio A (cyc)	46	video + photo, lighting grid
4	Control / edit	13	2 seats, glass to both rooms
5	Podcast booth	18	4 seats + cameras, room-in-room
6	Green room	8	suite entry, guest wait
7	Sound lock + make-up	7	acoustic double doors
8	Kit store	5	lights, cameras, props
9	Library	43	thinking + reading, no calls
10	Wellness / parent room	5	lockable, sink, fridge
11	Prayer (women)	6	6 to 8
12	Prayer (men)	9	10 to 12
Core: stairs, lift, WCs, services		95	identical on every floor
Corridors and lobbies		32	

FLOOR DATA	
Gross floor area	390 m² (4,198 sq ft)
Usable, excluding core	295 m²
Floor to floor	4.2 m
Desks on this floor	18

- DESIGN MOVES**
- One suite, one door.** Guests walk from the lift into the green room without crossing the creative floor.
 - Shared control room.** The cyc studio and the room-in-room podcast booth both sit behind glass from one control desk.
 - The core is the buffer.** Studio noise on one side, library and prayer on the other.
 - No glare.** Creative clusters run at right angles to the glass.

- SPECIFICATION NOTES**
- Studio and podcast booth: room-in-room on isolation mounts, no windows, own quiet AC zone with lined ducts.
 - Studio power on its own distribution board; DMX lighting grid at about 3.2 m.
 - Library at NC 30 or lower. Its wall to the creative floor is an acoustic partition lined with books.
 - Prayer rows set to the qibla (277.6° from true north in Dhaka). Wudu taps with floor drains in the WCs next door.

LEGEND

Community & hospitality

Meet & collaborate

Workspace

Studio & tech ops

Leadership

Quiet & wellbeing

Core & services

Circulation

Structure / core wall

Partition

Glazed partition

Acoustic wall (studio)

Door swing

Column, 5.2 m grid

KEY

L2

L1

G

0 1 2 3 4 5 m

SCALE 1:100 AT A3

Plate assumed 26 x 15 m on a 5.2 m grid. Refit to the real building once measured. Furniture indicative.

The Engine Room



ROOM SCHEDULE			
No.	Room	m²	Use / capacity
1	Engineering	95	24 desks incl. tech lead + 4 pods
2	War room	18	8 seats, whiteboard walls
3	Director	18	1 + 4 visitors
4	CEO	20	1 + 4 at table
5	Exec zone + EA	20	EA desk, print, storage
6	Pantry	10	sink, fridge, 6 stools
7	NOC / command centre	40	6 seats, video wall, glass to corridor
8	Tech bench	12	2 ESD benches, build + repair
9	MDF comms room	9	2 racks, own AC (N+1), UPS
10	IT store	6	devices, spares
Core: stairs, lift, WCs, services		95	identical on every floor
Corridors and lobbies		46	

FLOOR DATA	
Gross floor area	390 m² (4,198 sq ft)
Usable, excluding core	295 m²
Floor to floor	3.6 m
Desks on this floor	33

- DESIGN MOVES
- Lead from inside the team.** The tech lead (TL) sits at the head of squad B beside the war room. No closed office.
 - A pod closes every cluster.** Calls leave the desk without leaving the team.
 - Visible operation.** The NOC sits behind glass on the corridor. The racks stay locked away.
 - Quiet east end.** Leadership with an EA desk. Visitors are met downstairs.

- SPECIFICATION NOTES
- MDF: two 42U racks, N+1 cooling, 30-minute UPS, clean-agent fire suppression, card and PIN entry.
 - NOC: video wall on the blank west wall, own UPS circuit, lighting zone for night shifts.
 - Power and Cat6A data at every desk, monitor arms, sit-stand desks for at least a quarter of the seats.
 - CEO, director and war room at STC 45. Whiteboard paint wall to wall in the war room.

LEGEND

Community & hospitality

Meet & collaborate

Workspace

Studio & tech ops

Leadership

Quiet & wellbeing

Core & services

Circulation

Structure / core wall

Partition

Glazed partition

Acoustic wall (studio)

Door swing

Column, 5.2 m grid

KEY

L2

L1

G

0 1 2 3 4 5 m

SCALE 1:100 AT A3

Plate assumed 26 x 15 m on a 5.2 m grid. Refit to the real building once measured. Furniture indicative.

What the building holds

Every room on every floor, with the numbers checked against published planning benchmarks.

Floor	Room	m²	sq ft	Use / capacity
G	Arrival hall + reception	60	640	host desk, 2 meeting pods
	Forum / town hall	94	1,008	~75 seated, ~100 with lobby
	Work café	60	640	28 seats, power at every seat
	Boardroom	28	297	10 seats
	Meeting	11	116	6 seats
	Interview / vetting	7	78	3 seats, partner assessments
	Core (stairs, lift, WCs, services)	95	1,026	
	Corridors and lobbies	36	392	
	The Commons total (gross)	390	4,198	
L1	Creative & media studio	87	935	16 desks, pin-up wall
	Creative review	15	159	6 seats, colour-calibrated screen
	Studio A (cyc)	46	494	video + photo, lighting grid
	Control / edit	13	136	2 seats, glass to both rooms
	Podcast booth	18	199	4 seats + cameras, room-in-room
	Green room	8	90	suite entry, guest wait
	Sound lock + make-up	7	78	acoustic double doors
	Kit store	5	56	lights, cameras, props
	Library	43	465	thinking + reading, no calls
	Wellness / parent room	5	52	lockable, sink, fridge
	Prayer (women)	6	67	6 to 8
	Prayer (men)	9	93	10 to 12
	Core (stairs, lift, WCs, services)	95	1,026	
	Corridors and lobbies	32	348	
	The Studio total (gross)	390	4,198	
L2	Engineering	95	1,025	24 desks incl. tech lead + 4 pods
	War room	18	198	8 seats, whiteboard walls
	Director	18	198	1 + 4 visitors
	CEO	20	217	1 + 4 at table
	Exec zone + EA	20	217	EA desk, print, storage
	Pantry	10	103	sink, fridge, 6 stools
	NOC / command centre	40	427	6 seats, video wall, glass to corridor
	Tech bench	12	127	2 ESD benches, build + repair
	MDF comms room	9	101	2 racks, own AC (N+1), UPS
	IT store	6	62	devices, spares
	Core (stairs, lift, WCs, services)	95	1,026	
	Corridors and lobbies	46	495	
	The Engine Room total (gross)	390	4,198	
	Building total (gross)	1,170	12,594	3 floors

CAPACITY

52

Assigned desks
24 engineering, 6 NOC, 16 creative, 2 studio control, CEO, director, EA, host

28

Partner and client seats
work café, power at every seat

33

Meeting-room seats
boardroom 10, war room 8, meeting 6, review 6, interview 3

8

Pods
5 phone pods and 1 duo pod upstairs, 2 meeting pods in the lobby

~100

Town hall
about 75 seated (30 on the steps), the rest standing in the arrival hall

20

Prayer places
men up to 12, women up to 8, wudu in the L1 WCs

1

Content studio suite
cyc studio, 4-seat podcast booth, control room

SPACE MIX

Use	G	L1	L2	Total m²	Share
Workspace	-	87	95	182	16%
Meet & collaborate	46	15	18	79	7%
Community & hospitality	213	-	10	222	19%
Studio & tech ops	-	98	67	164	14%
Leadership	-	-	59	59	5%
Quiet & wellbeing	-	63	-	63	5%
Core & services	95	95	95	286	24%
Circulation	36	32	46	115	10%
Total	390	390	390	1,170	100%

BENCHMARK CHECK

Measure	Benchmark	This scheme
Phone and focus pods	1 per 6 to 12 staff (Gable, 2026)	6 staff pods for 52 people: 1 per 9
Meeting room mix	Huddle 40 to 50%, small 25 to 35%, large 15 to 20% (CoworkingCafe)	4 huddle, 2 small, 2 large: 50 / 25 / 25%. Large runs 5 points over (see note)
Large rooms	80% of meetings have 6 people or fewer (CoworkingCafe)	Only 2 rooms seat more than 6; no second boardroom
Gross area per desk	150 to 250 sq ft is average density (OfficeSpace, 2026)	242 sq ft, including studio, forum and café
Toilets per floor	BNBC Table 8.6.1: 1 WC per 25 men, 1 per 15 women, 1 basin per 25, a service sink, an accessible WC	3 WC women, 2 WC and 2 urinals men, 4 basins, accessible WC, cleaner sink: comfortably covers 45 people
Clear height	BNBC Part 3: at least 2.44 m in air-conditioned rooms	About 2.9 m on L2, more below

Read: the scheme sits inside the benchmarks with one deliberate exception. Large rooms run 5 points over because one is the client boardroom and the other the squads' war room. Area per desk sits near the top of the range because the studio, forum and café are revenue and brand assets, not overhead.

EFFICIENCY AND FLEX

- 1** **Net to gross 76%.** Each floor gives 295 m² of usable space out of 390 m². The core takes 95 m², normal for a small plate with two stairs.
- 2** **Room to grow on L2.** Trade the four cluster-end pods for one more desk pair per cluster: 8 more desks, no walls move.
- 3** **Hybrid headroom.** At a conservative 1.2 people per desk (Asia Pacific averages 1.3, OfficeSpace 2026), 52 desks support about 62 staff.

What it takes to build

Targets to hand an interior architect, a budget band at 2026 Dhaka rates, and the five moves that unlock the next draft.

BUILDING AND ENGINEERING STANDARDS

Topic	Target in this scheme	Basis
Heights	G 4.5 m, L1 4.2 m, L2 3.6 m floor to floor. About 2.9 m clear on work floors and 3.5 m in the studio, so keep deep beams out of the studio bay.	<i>BNBC Part 3: 2.44 m minimum clear in air-conditioned business rooms</i>
Toilets	Per floor: 3 WC women, 2 WC and 2 urinals men, 4 basins, accessible WC with shower, cleaner sink.	<i>BNBC Table 8.6.1, offices</i>
Fire and escape	Two protected stairs about 13 m apart: 1.15 m flights, 279 mm goings, risers 178 mm or less. Travel to a stair under 25 m from any point. Smoke detection, emergency lighting, sprinklers recommended, speed gates release on alarm.	<i>BNBC Part 4 Tables 4.3.5 to 4.3.8: 1.12 m minimum, 60 m travel for business use. Architect to confirm separation with the Fire Service</i>
Room acoustics	Meeting rooms and executive offices STC 45, NC 30. Boardroom and other video-call rooms STC 53, NC 25. Open plan NC 40 with NRC 0.90 ceilings.	<i>GSA and ASHRAE guidance</i>
Studio acoustics	Room-in-room podcast booth and studio, STC 60+ envelope, NC 15 to 20, RT60 0.2 to 0.4 s, acoustic doors, lined low-velocity ducts.	<i>Studio practice; appoint an acoustic consultant</i>
Lighting	500 lux and UGR 19 or lower at desks, 100 lux minimum in corridors. Studio on flicker-free LED, CRI 95+, DMX grid.	<i>EN 12464-1</i>
Air	VRF cooling with dedicated fresh air (ERV), CO2 under 1,000 ppm, MERV 13 filters for Dhaka dust. MDF on its own N+1 cooling.	<i>ASHRAE 62.1 ventilation rates</i>
Power and IT	Full generator backup. Online UPS for MDF and NOC (30 min). Dual ISP plus BDIX, fibre riser, Cat6A, Wi-Fi 7 (about 3 access points per floor). Card access at gates, studio and tech ops. CCTV.	<i>Dhaka grid reality. An IT governance firm has to run a clean house.</i>
Access	Step-free entry, lift to all floors, 900 mm clear doors, accessible WC on every floor.	<i>BNBC accessibility provisions</i>
Climate	Shade south and west glass, low-E double glazing. Put blank walls (LED wall, studio, MDF) on the hot side once orientation is known.	<i>Dhaka sun and heat load</i>

ROOMS THAT DRIVE COST AND RISK

Room	Size	Non-negotiables
Studio A (cyc)	46 m², 3.5 m clear	Two-wall cyc, DMX lighting grid, own power board, own quiet AC zone, no windows.
Podcast booth	18 m²	Room-in-room on isolation mounts, two cameras, acoustic window to the control room, NC 15 to 20.
MDF comms room	9 m²	Two 42U racks, N+1 cooling, 30-minute UPS, clean-agent suppression, card and PIN.
NOC	40 m²	6 seats facing a video wall on the blank west wall, own UPS circuit, glass to the corridor.
Forum	94 m²	Stage at +300 mm, 4.2 x 2.4 m LED wall, 3-tier step seating with chair store, DMX dimming.

FIT-OUT BUDGET BAND

Scenario, 12,594 sq ft	BDT per sq ft	Total, BDT crore
Mid-range throughout	1,500 to 2,800	1.9 to 3.5
Premium throughout	3,000 to 5,500	3.8 to 6.9
Recommended: premium on G and L1, mid-range on L2		3.1 to 5.8

Rates: House De Arch Bangladesh fit-out guide (June 2026). Typical split: furniture 35 to 42%, construction 28 to 35%, MEP 12 to 18%, design and project management 8 to 12%, contingency 8 to 10%. Excludes the building shell, studio cameras and lights, and IT hardware. Early estimates move by up to 30% until a bill of quantities exists.

ASSUMPTIONS BEHIND THIS DRAFT

- No building dimensions were given. Planned on a 26 x 15 m plate: 390 m² (4,198 sq ft) per floor, 1,170 m² (12,594 sq ft) in total. The 15 m depth is what lets code-compliant stairs climb a 4.5 m ground floor.
- Side walls assumed open for windows and the forum side exit. On a party wall, both move to the street front.
- Street on the long side; compass orientation unknown.
- New build or full-building control, so floor heights can be set. In leased floors the landlord fixes the core and heights: the zoning still holds, the step seating flattens and the studio needs at least 3.2 m clear.
- About 52 staff on site, plus up to 15 partners touching down.

NEXT FIVE MOVES

- Measure the real building.** Send the landlord or architect plan, or the plot size for a new build. The scheme gets refitted to the actual core and grid.
- Lock the 24-month headcount.** This draft carries 52 desks. L2 takes 8 more by trading the cluster-end pods for one more desk pair per cluster; no walls move.
- Appoint an interior architect** with this pack as the brief: design development, MEP drawings, bill of quantities.
- Bring in an acoustic consultant first.** The studio suite is the one thing that is expensive to fix once built.
- Phase it if cash is tight.** Ground and L2 first (clients and delivery), the L1 studio second.

Sources: BNBC Part 8 Table 8.6.1 and Part 3 (law.resource.org, BNBC 2012 text); BNBC 2015 final draft, Part 4 Tables 4.3.5 to 4.3.8 (anyflip); House De Arch, Office fit-out cost guide Bangladesh (2026); DataDrivenAEC, acoustic design requirements (GSA / ASHRAE); ProDec, recording studio acoustic guide; Gable, office phone booths (2026); CoworkingCafe, meeting room math; OfficeSpace, office space per person (2026).